


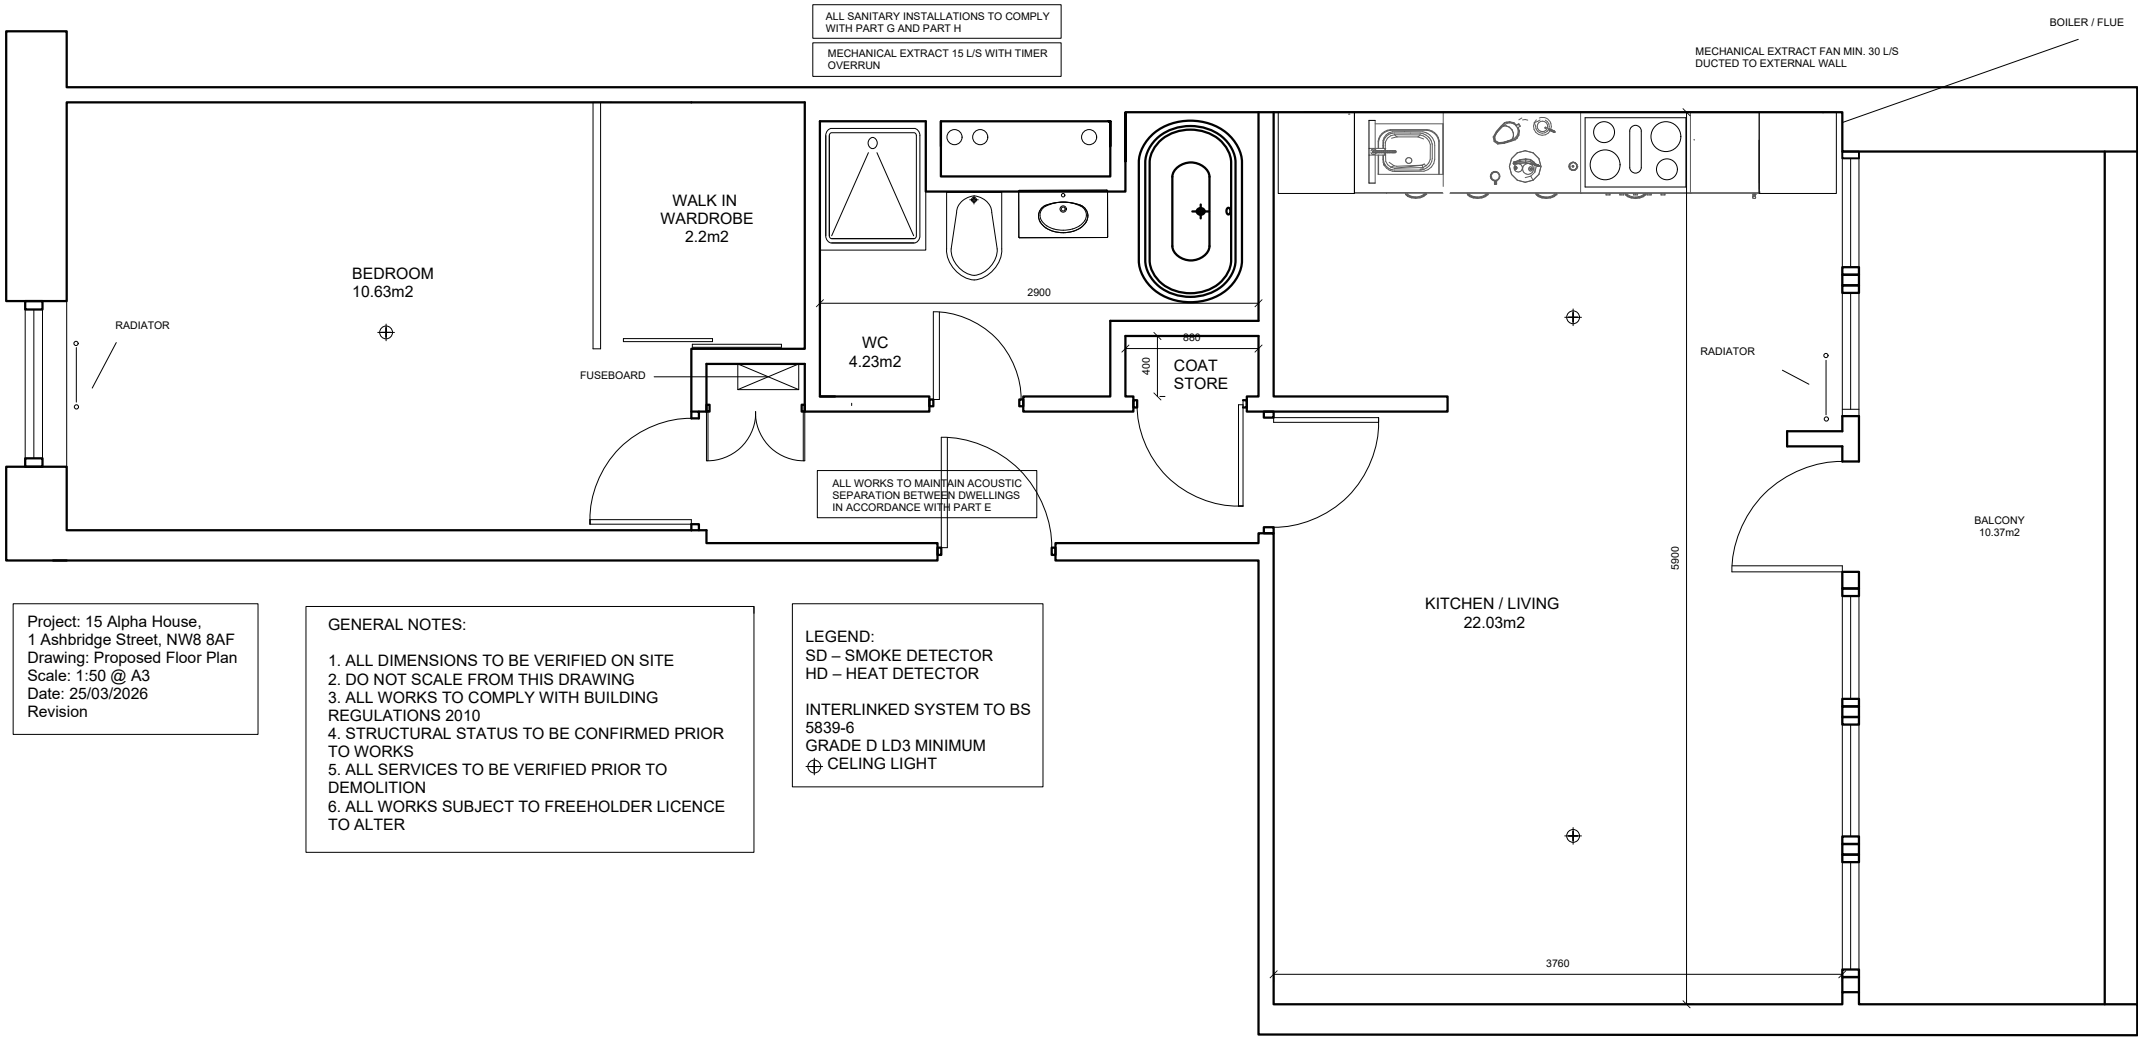

Project: 15 Alpha House,
1 Ashbridge Street, NW8 8AF
Drawing: Proposed Floor Plan
Scale: 1:50 @ A3
Date: 25/03/2026
Revision

- GENERAL NOTES:
1. ALL DIMENSIONS TO BE VERIFIED ON SITE
 2. DO NOT SCALE FROM THIS DRAWING
 3. ALL WORKS TO COMPLY WITH BUILDING REGULATIONS 2010
 4. STRUCTURAL STATUS TO BE CONFIRMED PRIOR TO WORKS
 5. ALL SERVICES TO BE VERIFIED PRIOR TO DEMOLITION
 6. ALL WORKS SUBJECT TO FREEHOLDER LICENCE TO ALTER

LEGEND:

SD – SMOKE DETECTOR
HD – HEAT DETECTOR

INTERLINKED SYSTEM TO BS 5839-6
GRADE D LD3 MINIMUM
⊕ CEILING LIGHT

